




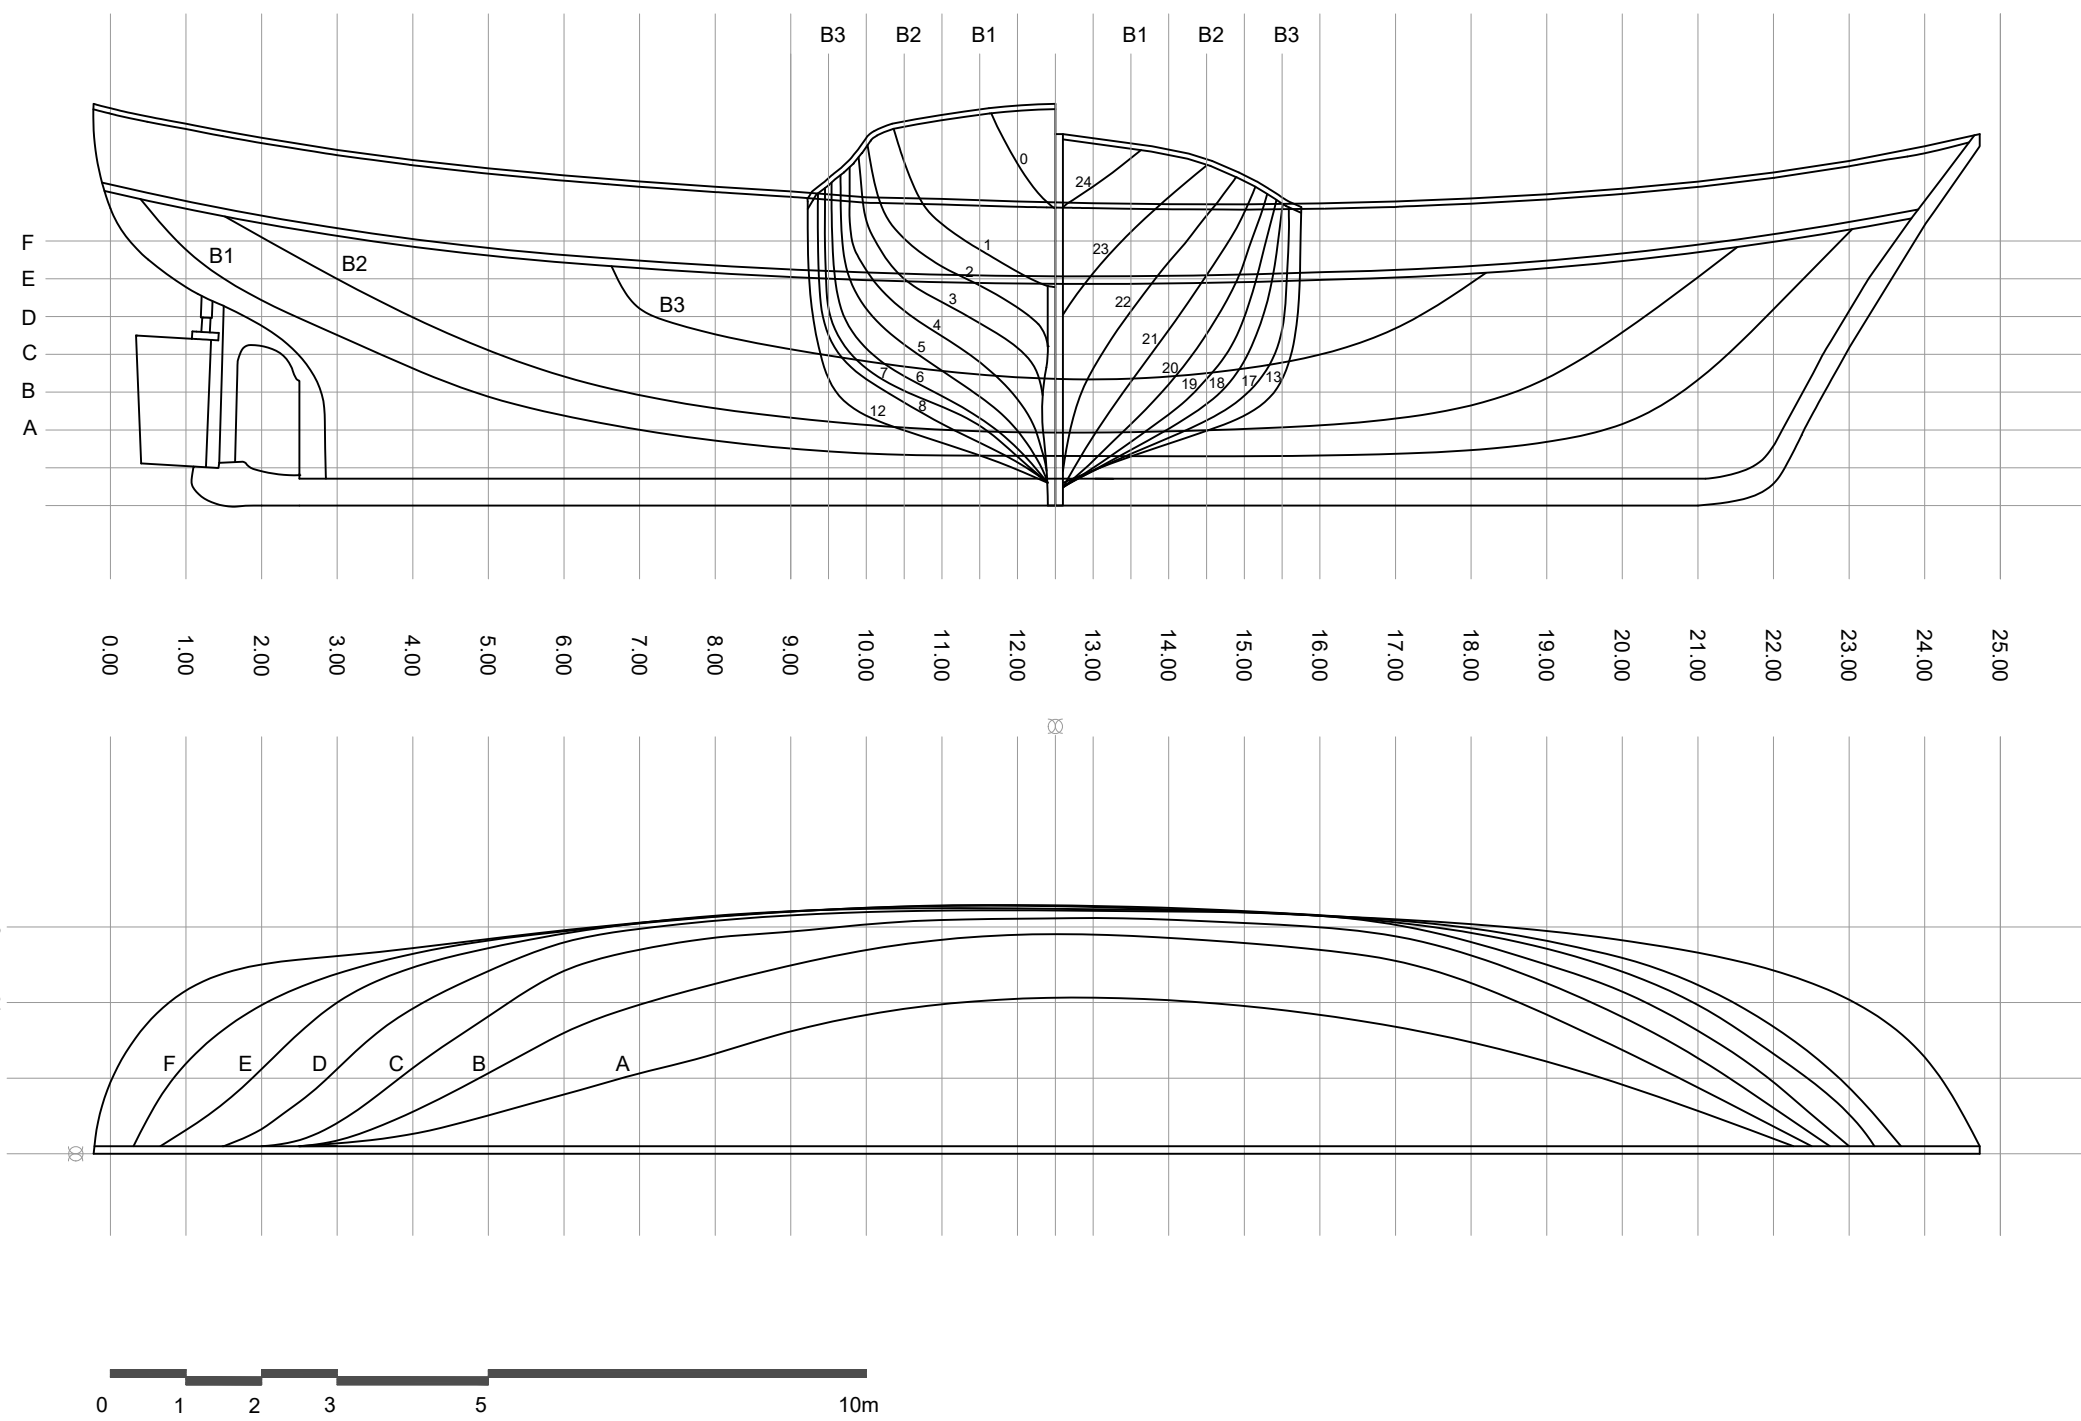


	Owner:	Municipality of Limassol	Monument Name:	Traditional Fishing Trawler "Lambousa"		
	Stakeholder:	Municipality of Limassol	Location:	34°39'41.7"N 33°01'27.9"E		
	Digitisation by:	UNESCO Chair on Digital Cultural Heritage, Cyprus University of Technology	Drawing Name:	Naval Lines		
			Scale:	1:100	Date:	April 2024

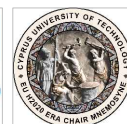

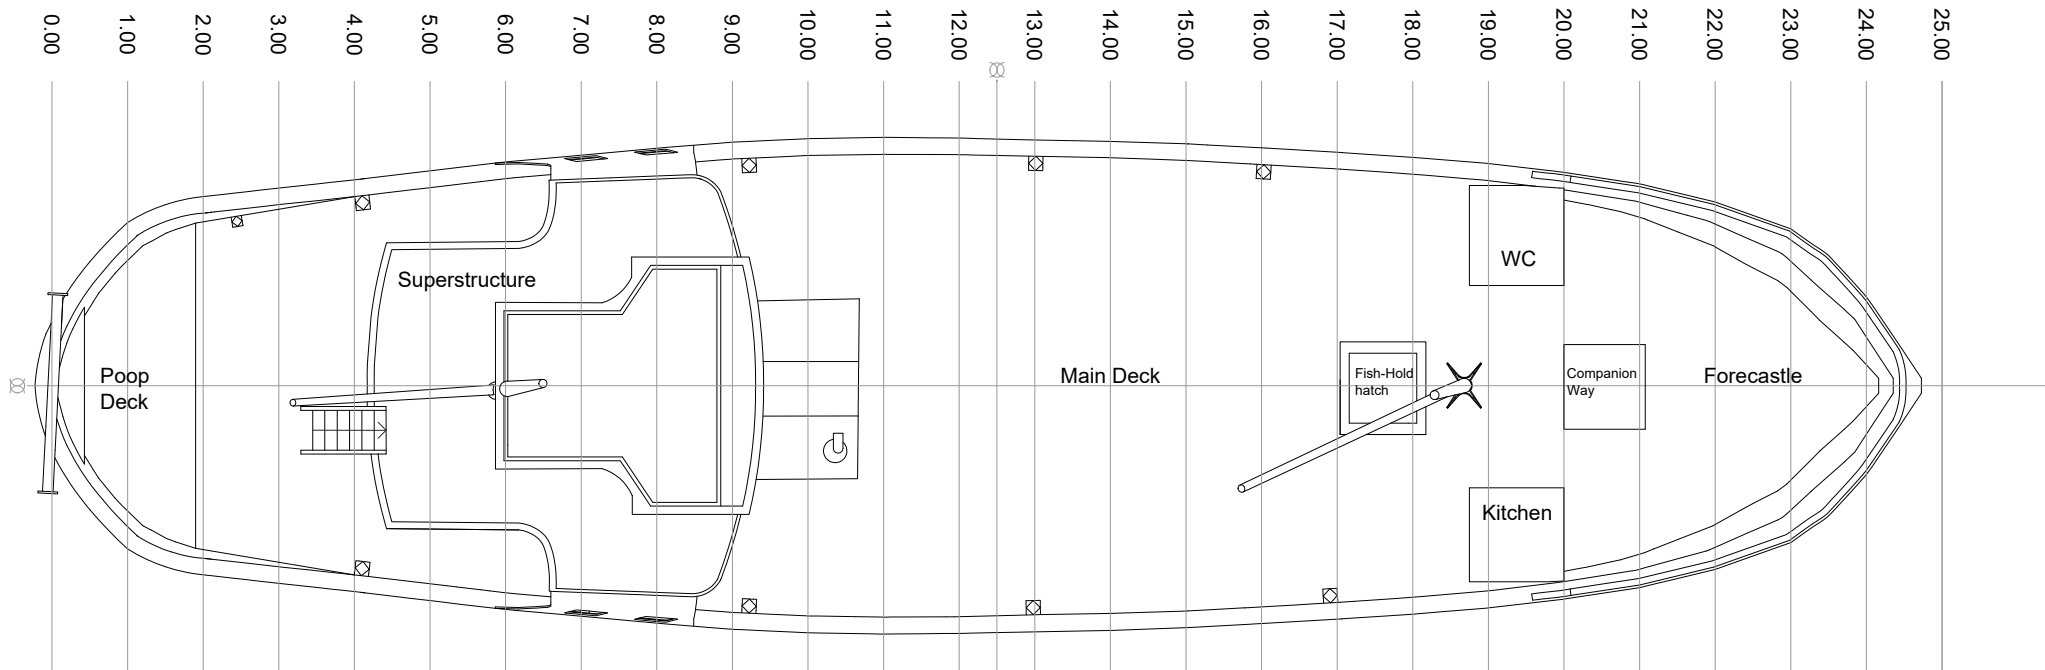

Top View

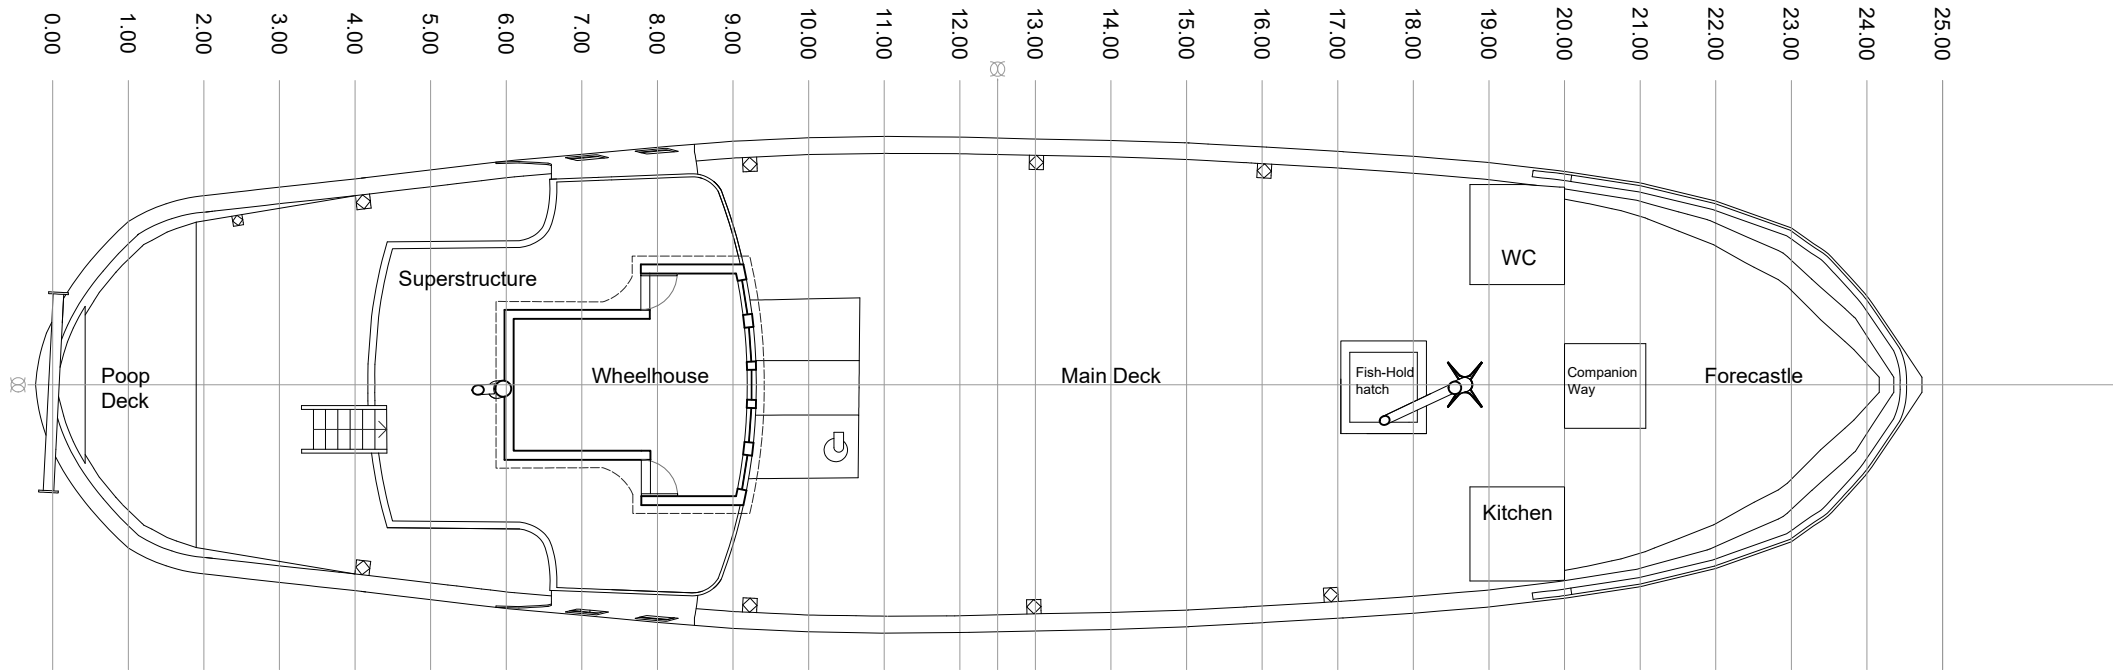


Plan View of Upper Deck - Level 6.60m




Owner:	Municipality of Limassol	Monument Name:	Traditional Fishing Trawler "Lambousa"			
Stakeholder:	Municipality of Limassol	Location:	34°39'41.7"N 33°01'27.9"E			
Digitisation by:	UNESCO Chair on Digital Cultural Heritage, Cyprus University of Technology	Drawing Name:	Floor Plans			
		Scale:	1:100	Date:	April 2024	



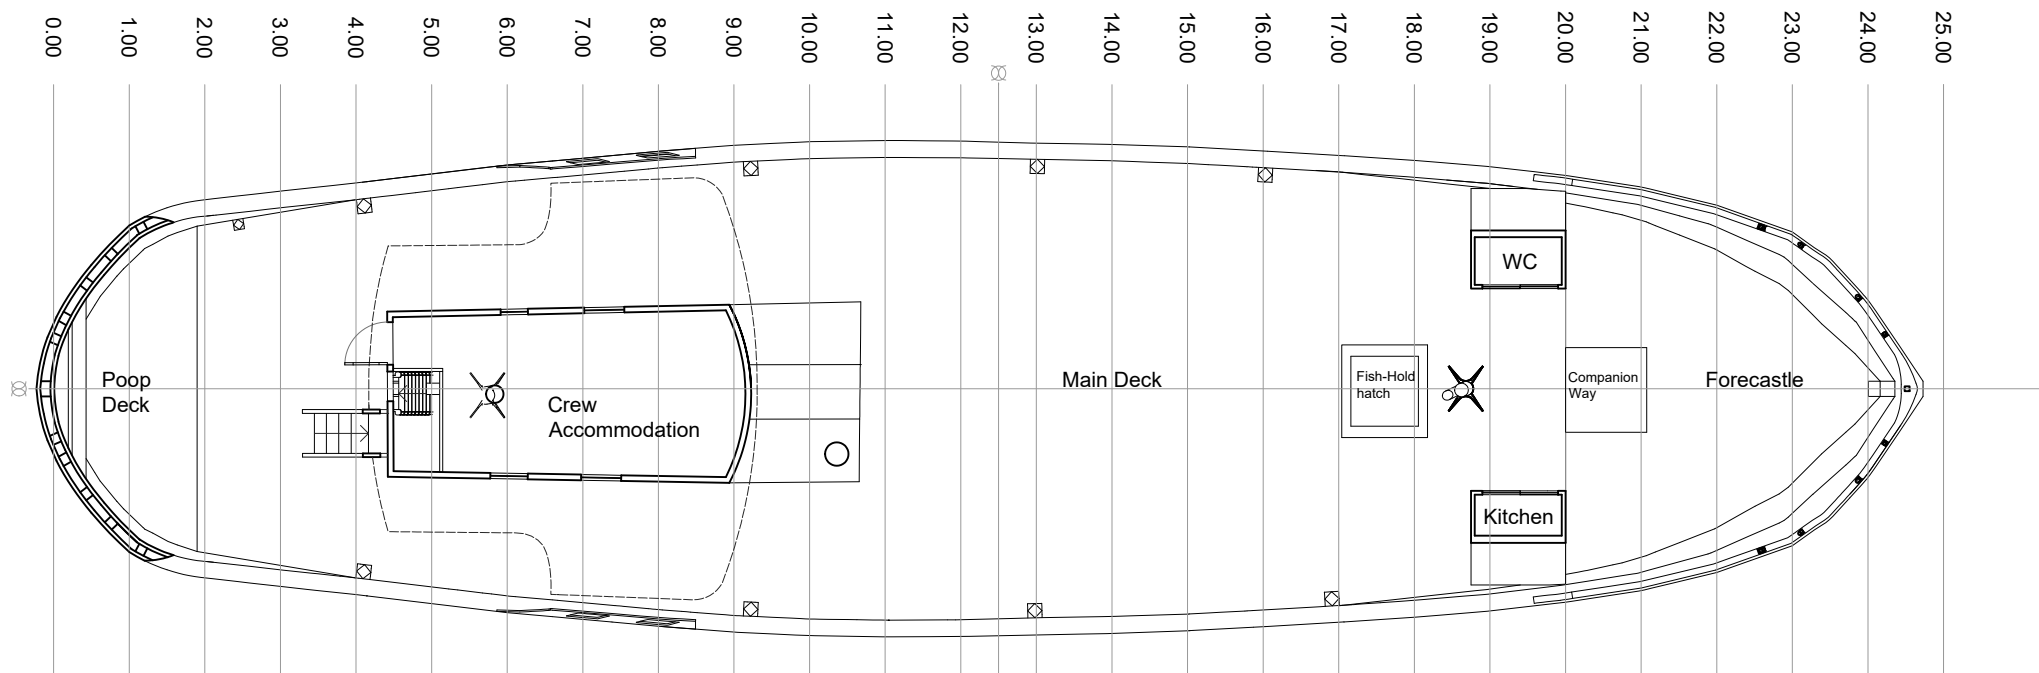


Plan View of Main Deck - Level 5.00m

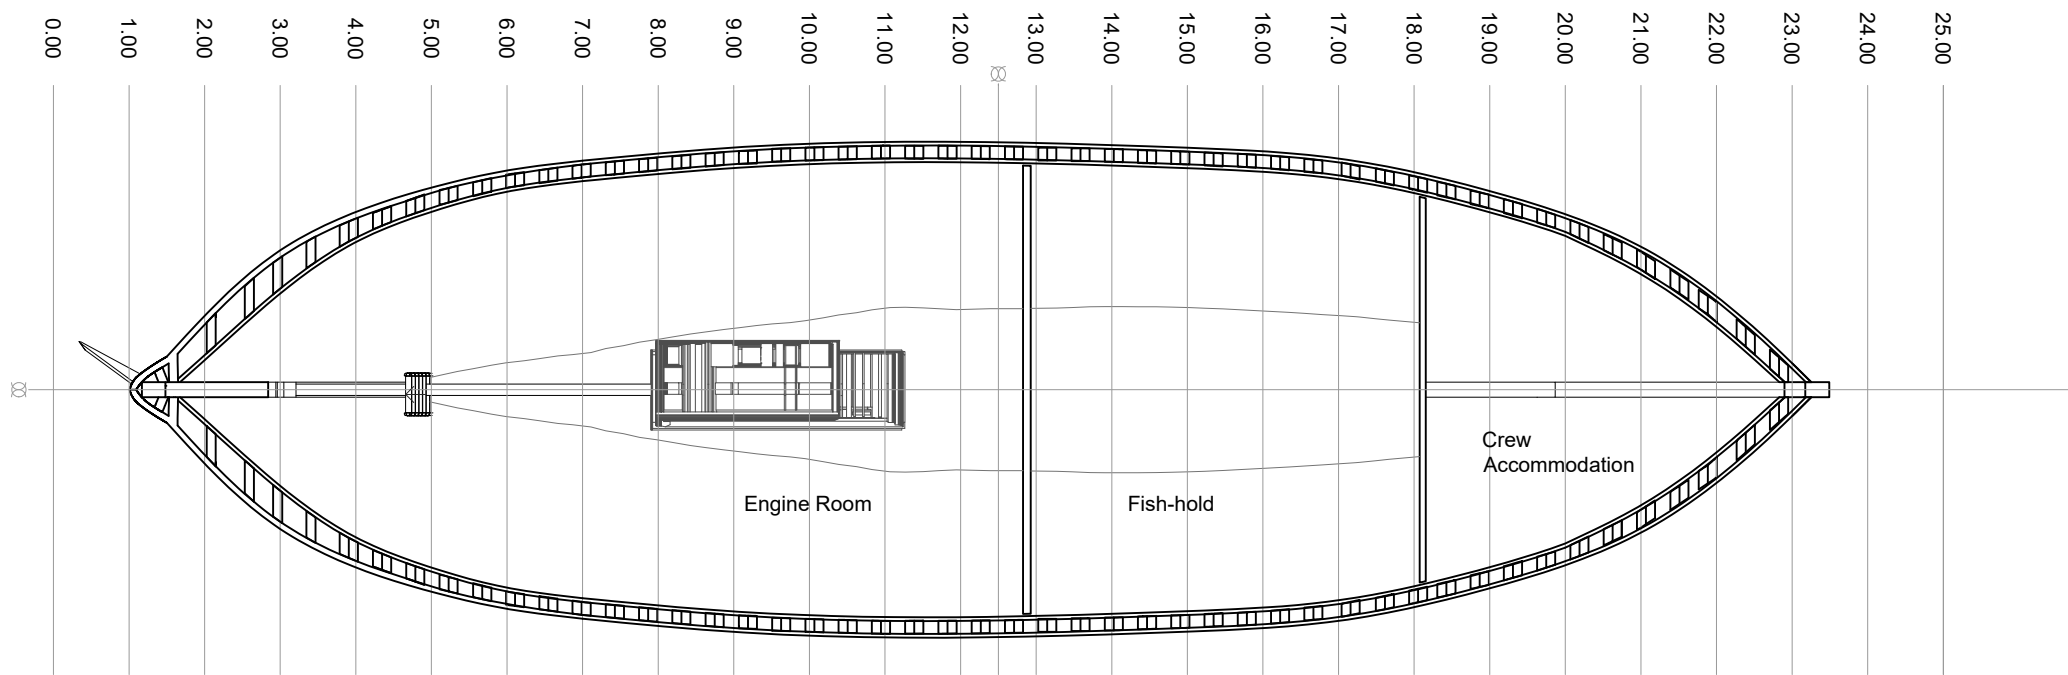

Plan View of Engine Room and Fish-Hold - Level 2.90m



	Owner:	Municipality of Limassol	Monument Name:	Traditional Fishing Trawler "Lambousa"		
	Stakeholder:	Municipality of Limassol	Location:	34°39'41.7"N 33°01'27.9"E		
	Digitisation by:	UNESCO Chair on Digital Cultural Heritage, Cyprus University of Technology	Drawing Name:	Floor Plans		
			Scale:	1:100	Date:	April 2024

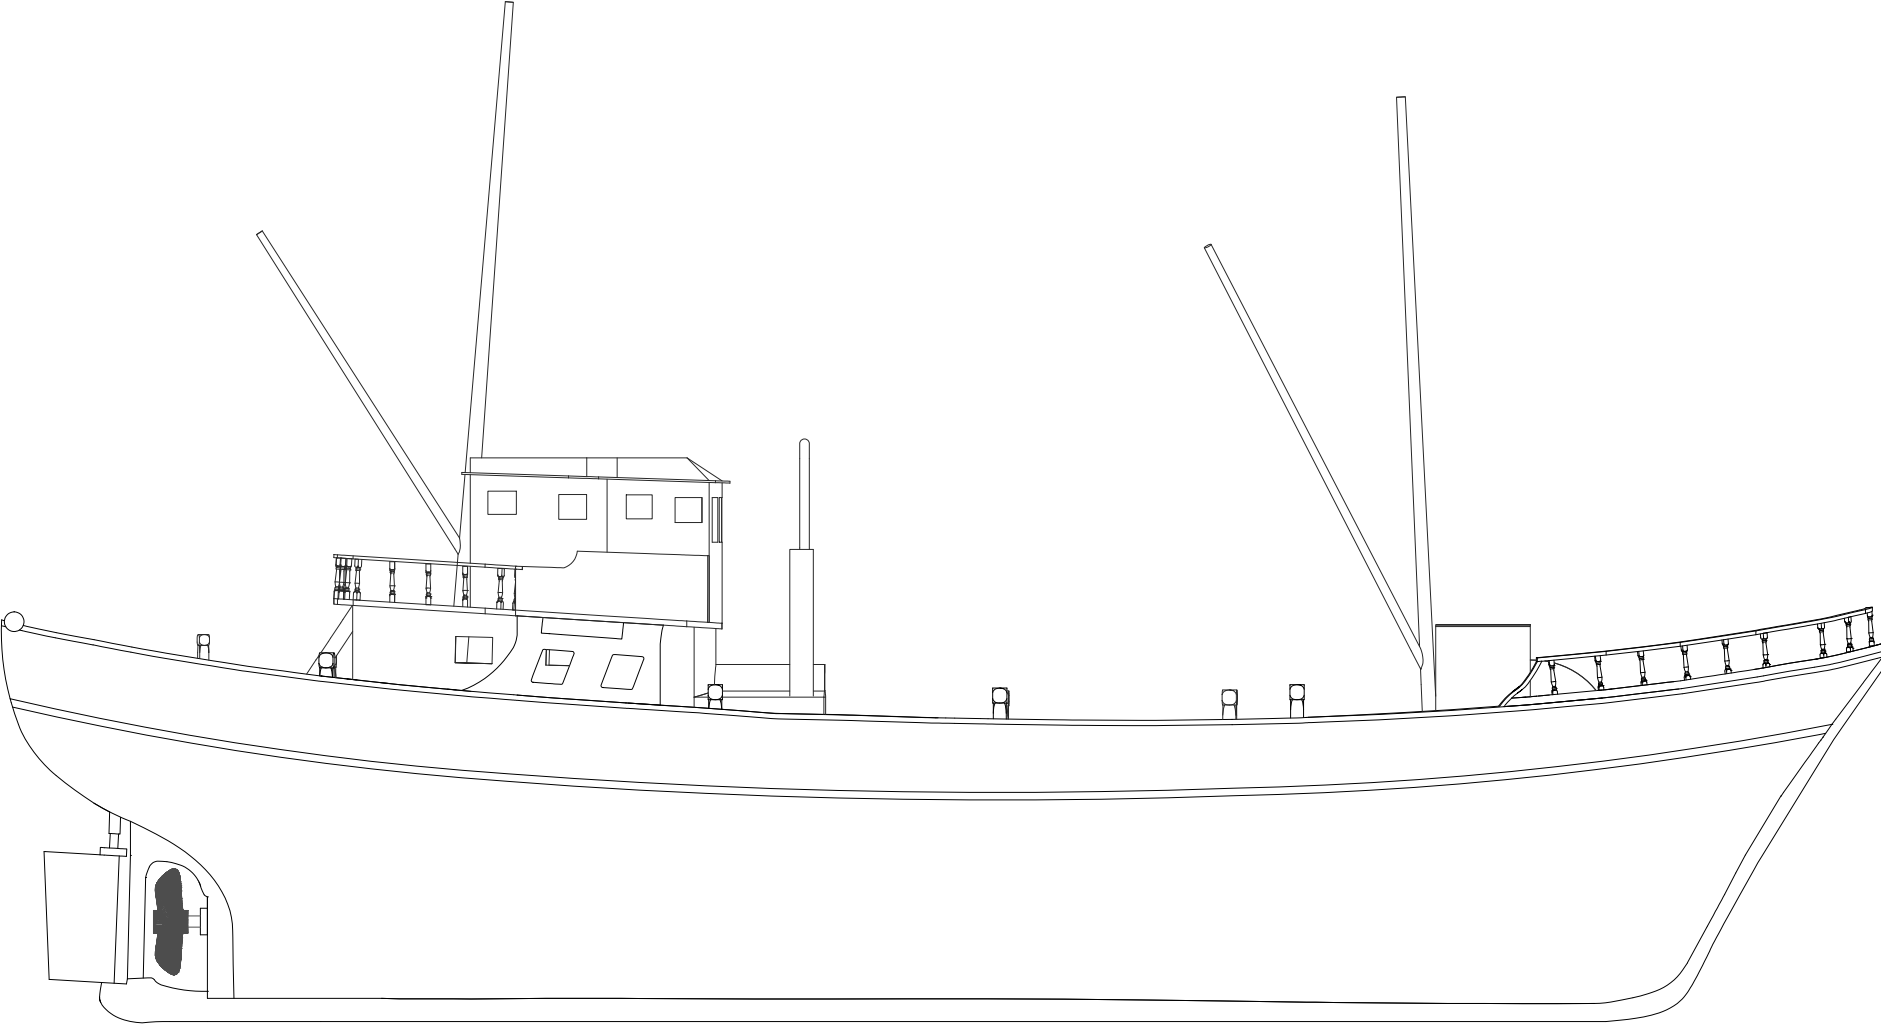


Profile




	Owner:	Municipality of Limassol	Monument Name:	Traditional Fishing Trawler "Lambousa"		
	Stakeholder:	Municipality of Limassol	Location:	34°39'41.7"N 33°01'27.9"E		
	Digitisation by:	UNESCO Chair on Digital Cultural Heritage, Cyprus University of Technology	Drawing Name:	Profile		
			Scale:	1:100	Date:	April 2024



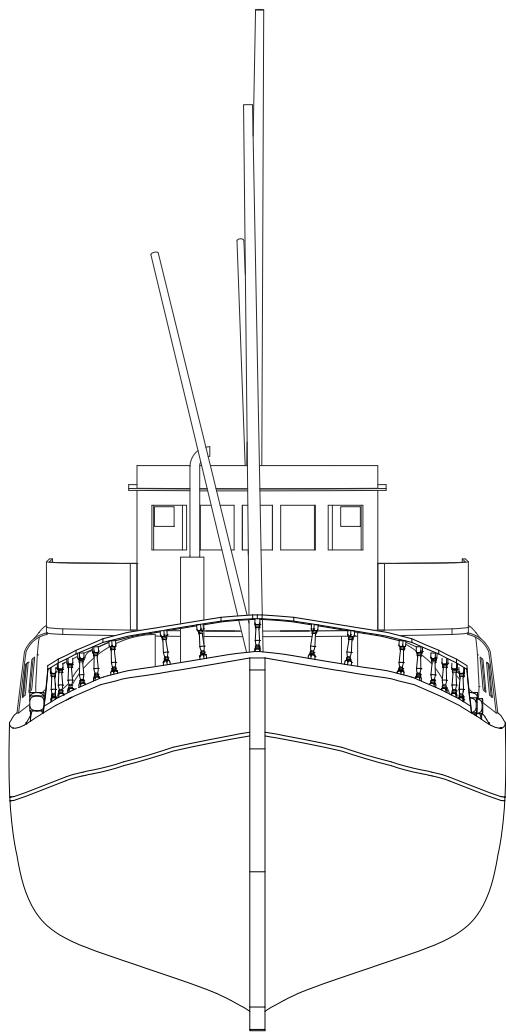

Bow View

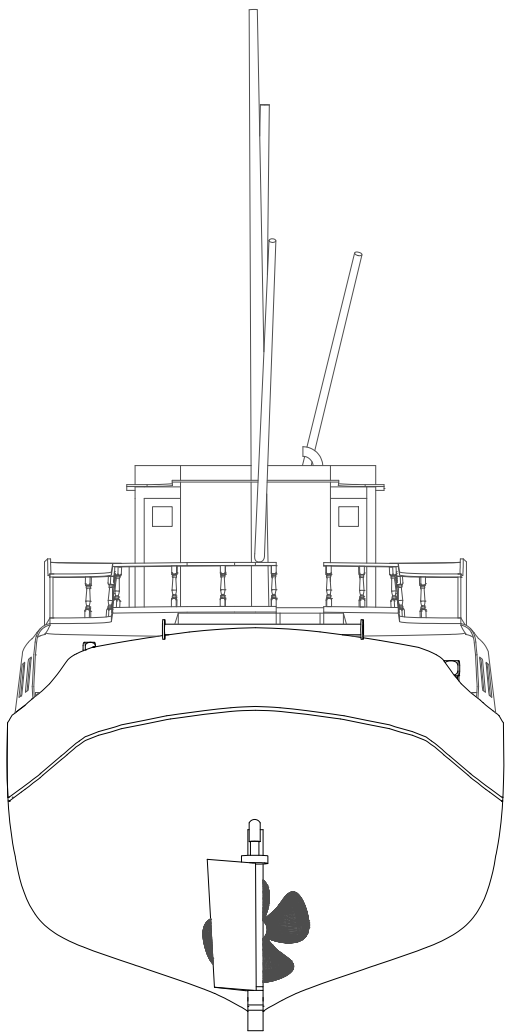


Stern View




	Owner:	Municipality of Limassol	Monument Name:	Traditional Fishing Trawler "Lambousa"		
	Stakeholder:	Municipality of Limassol	Location:	34°39'41.7"N 33°01'27.9"E		
	Digitisation by:	UNESCO Chair on Digital Cultural Heritage, Cyprus University of Technology	Drawing Name:	Bow and Stern View		
			Scale:	1:100	Date:	April 2024



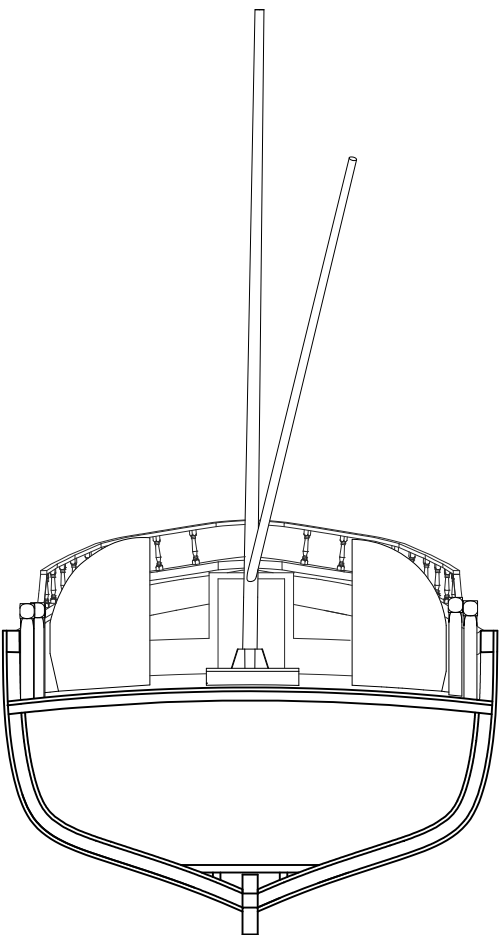

Cross Section (Bow)

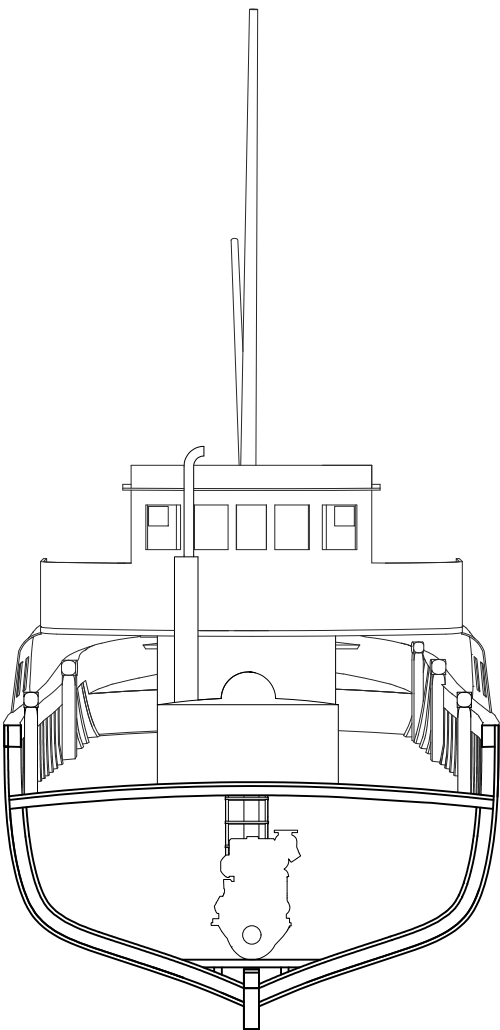


Cross Section (Stern)



	Owner:	Municipality of Limassol	Monument Name:	Traditional Fishing Trawler "Lambousa"		
	Stakeholder:	Municipality of Limassol	Location:	34°39'41.7"N 33°01'27.9"E		
	Digitisation by:	UNESCO Chair on Digital Cultural Heritage, Cyprus University of Technology	Drawing Name:	Cross Sections		
			Scale:	1:100	Date:	April 2024



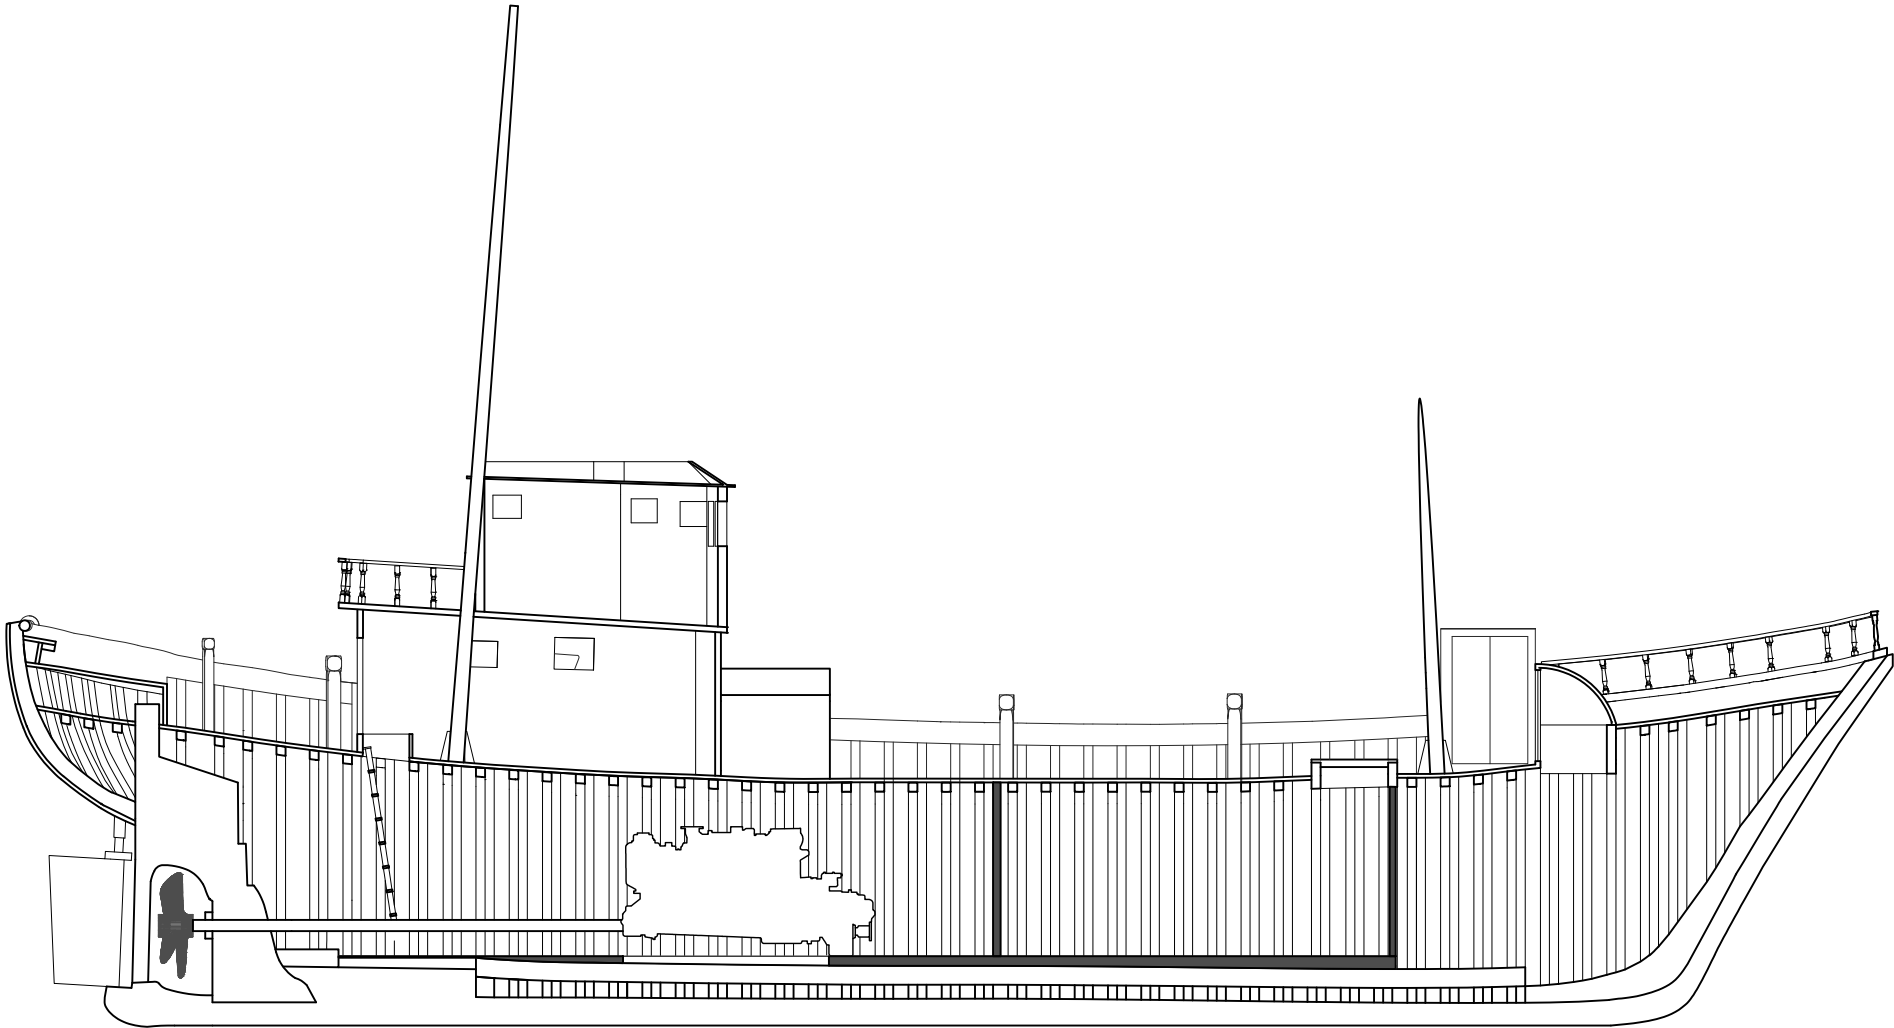

Longitudinal Section



	Owner:	Municipality of Limassol	Monument Name:	Traditional Fishing Trawler "Lambousa"		
	Stakeholder:	Municipality of Limassol	Location:	34°39'41.7"N 33°01'27.9"E		
	Digitisation by:	UNESCO Chair on Digital Cultural Heritage, Cyprus University of Technology	Drawing Name:	Longitudinal Section		
			Scale:	1:100	Date:	April 2024

